


A-101 FIRST FLOOR PLAN

RESIDENTIAL FLOOR PLAN

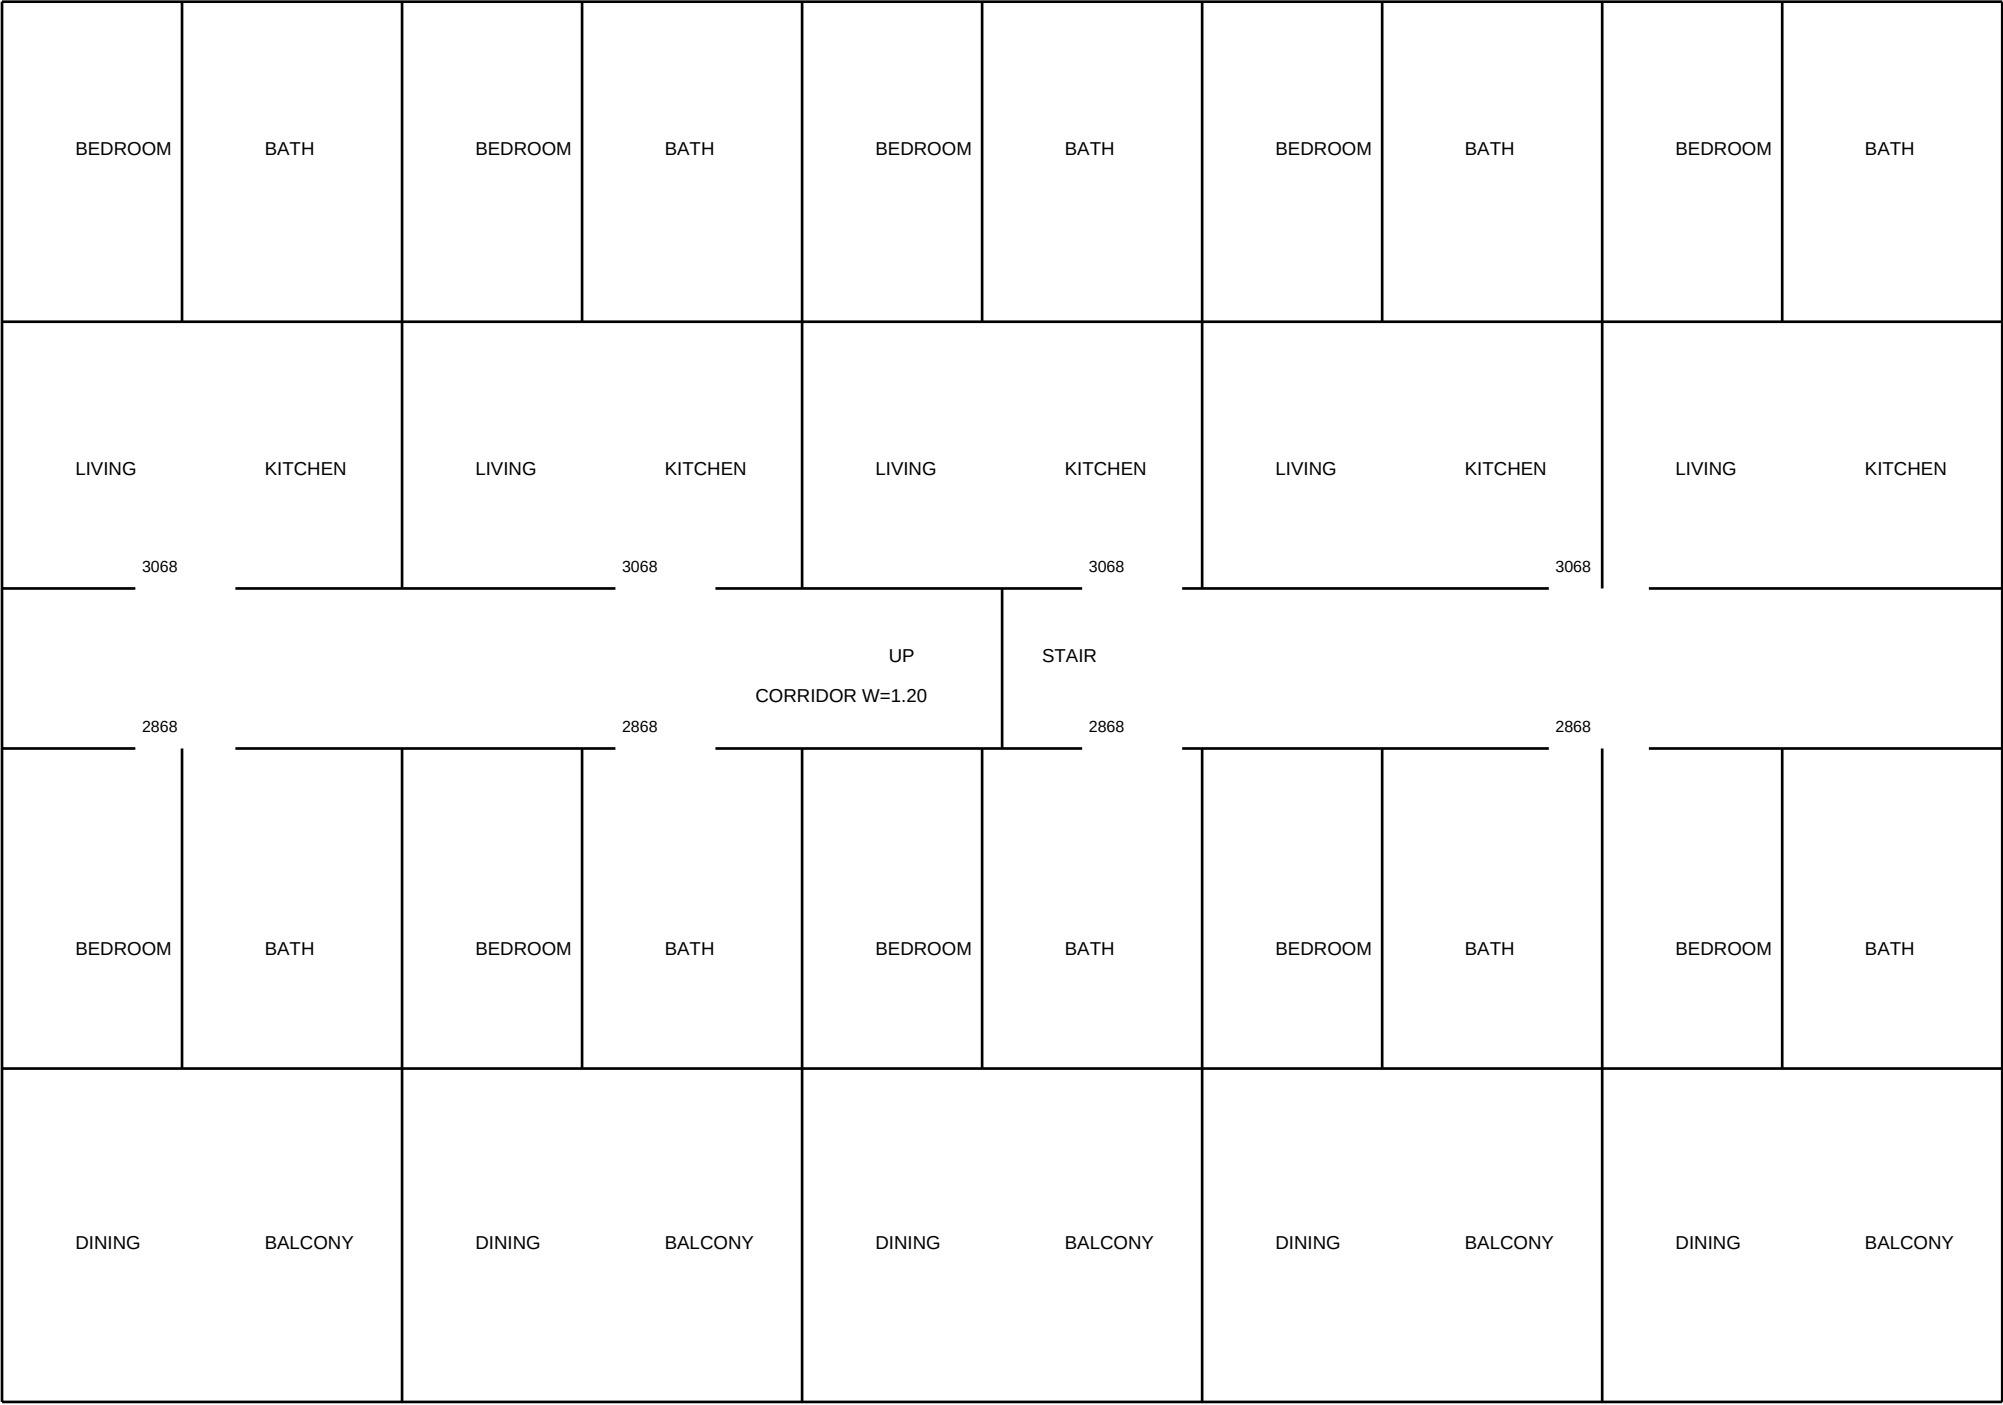


150'-0"

DOOR SCHEDULE / ROOM SCHEDULE / LEGEND

MARK	WIDTH	HEIGHT	ROOM	TYPE	NOTES
D01	3068	6'-8"	BEDROOM	SWING	SEE PLAN
D02	2868	6'-8"	BATH	SWING	SEE PLAN
D03	3068	6'-8"	BEDROOM	SWING	SEE PLAN
D04	2868	6'-8"	BATH	SWING	SEE PLAN
D05	3068	6'-8"	BEDROOM	SWING	SEE PLAN
D06	2868	6'-8"	BATH	SWING	SEE PLAN
D07	3068	6'-8"	BEDROOM	SWING	SEE PLAN
D08	2868	6'-8"	BATH	SWING	SEE PLAN
D09	3068	6'-8"	BEDROOM	SWING	SEE PLAN
D10	2868	6'-8"	BATH	SWING	SEE PLAN
D11	3068	6'-8"	BEDROOM	SWING	SEE PLAN
D12	2868	6'-8"	BATH	SWING	SEE PLAN

A-102 SECOND FLOOR PLAN


RESIDENTIAL FLOOR PLAN

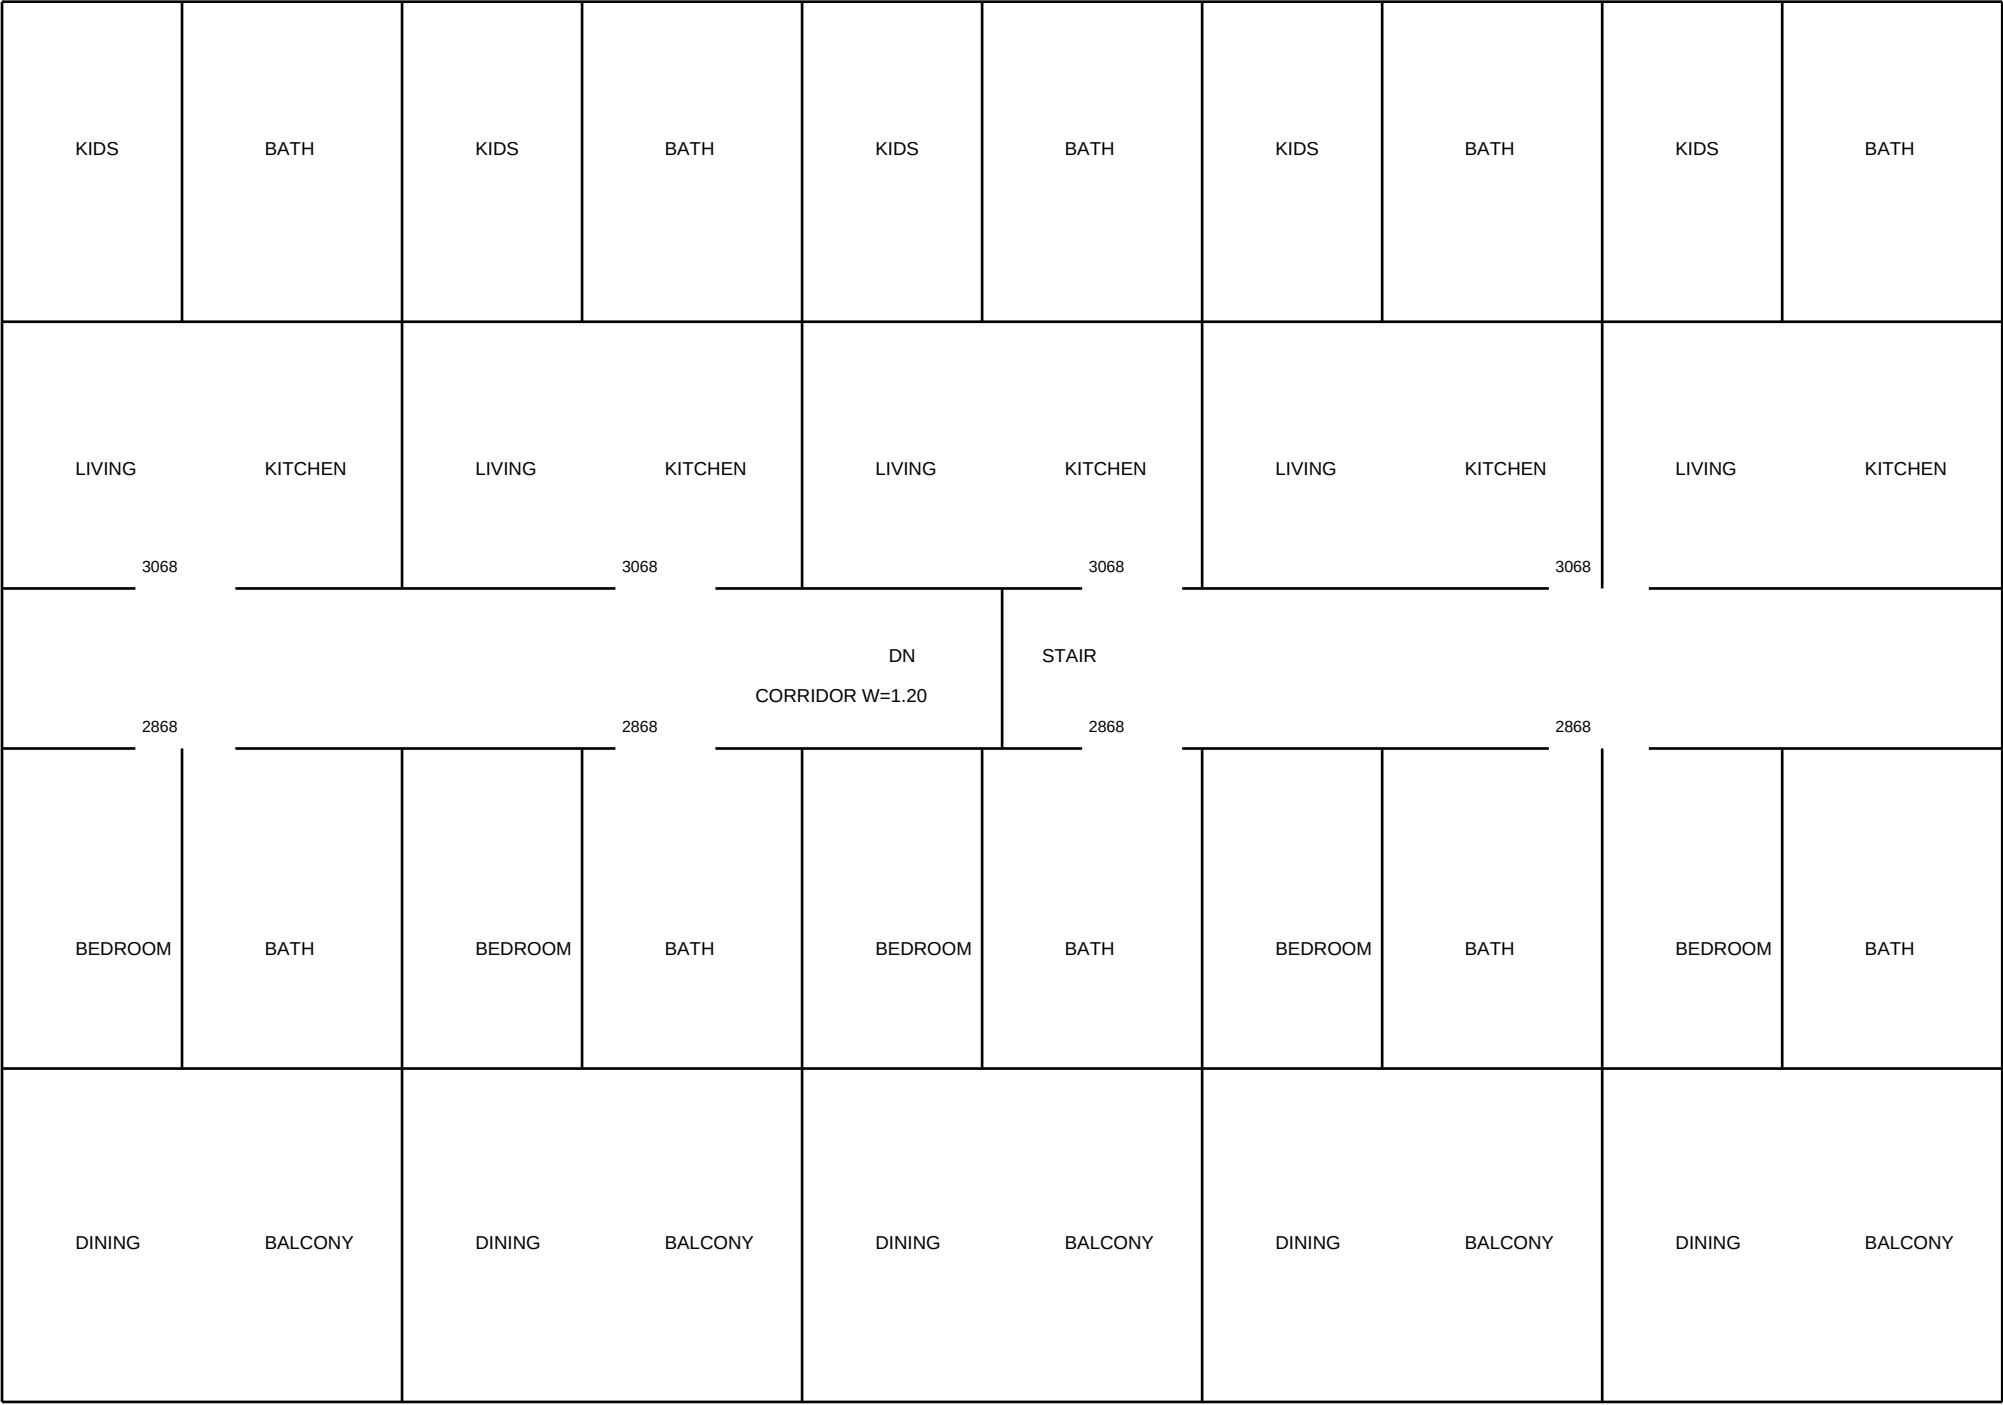

150'-0"

52'-6"

BUILDING ELEVATION AND SECTION

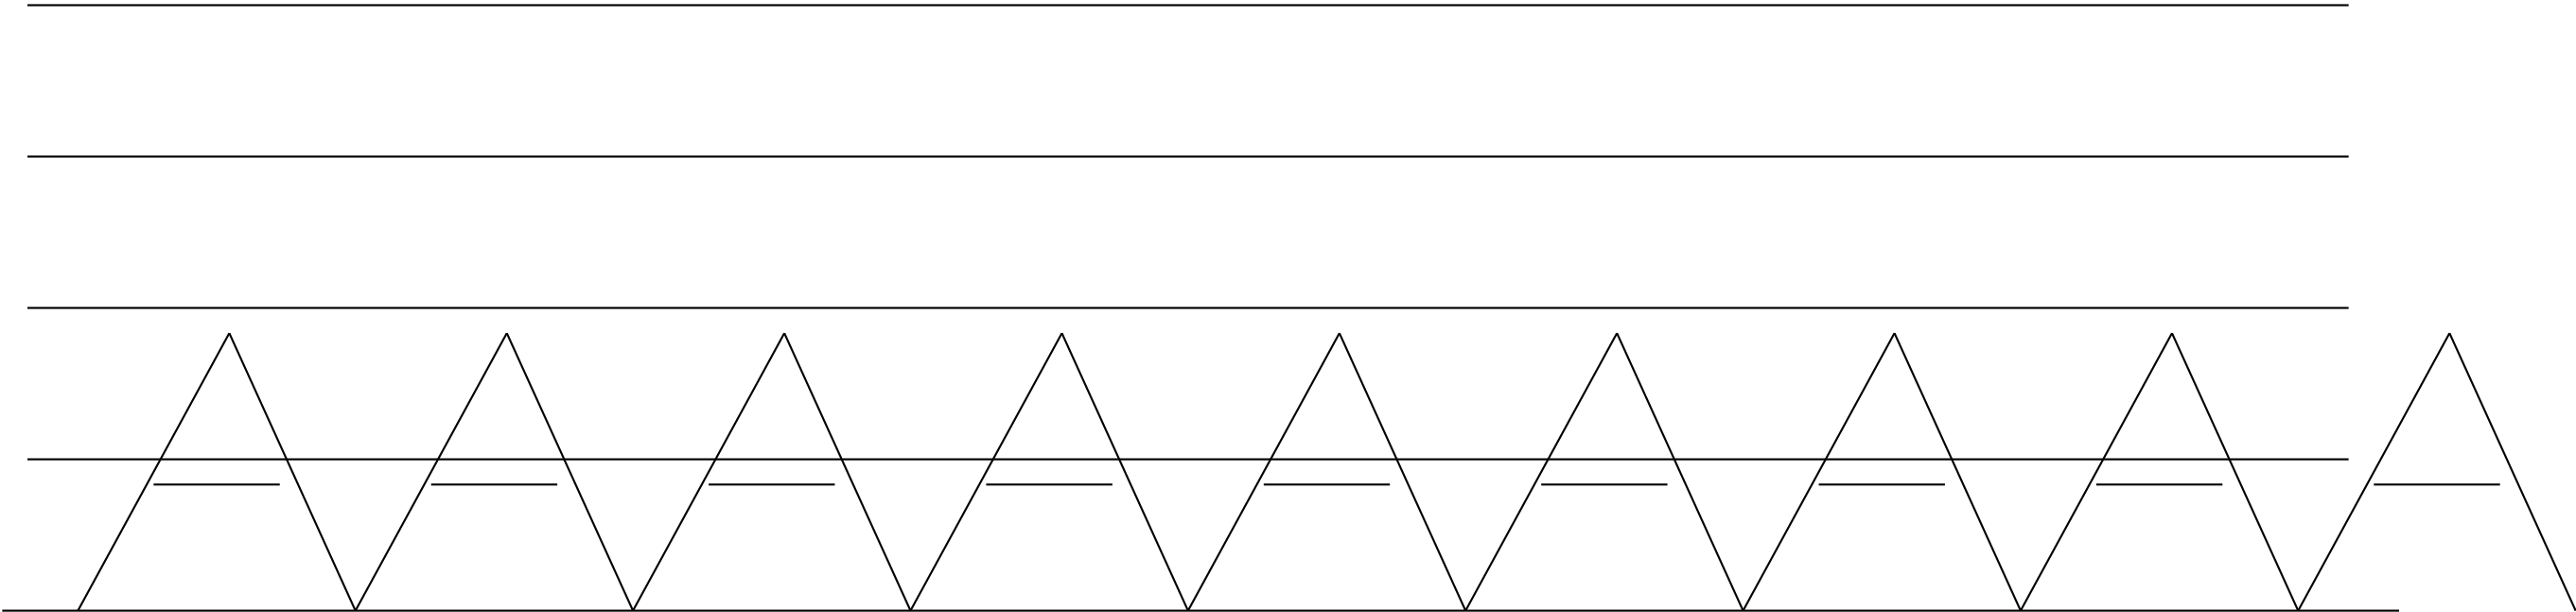

ELEVATION GRID

SECTION A-A

NOT A PLAN SHEET