




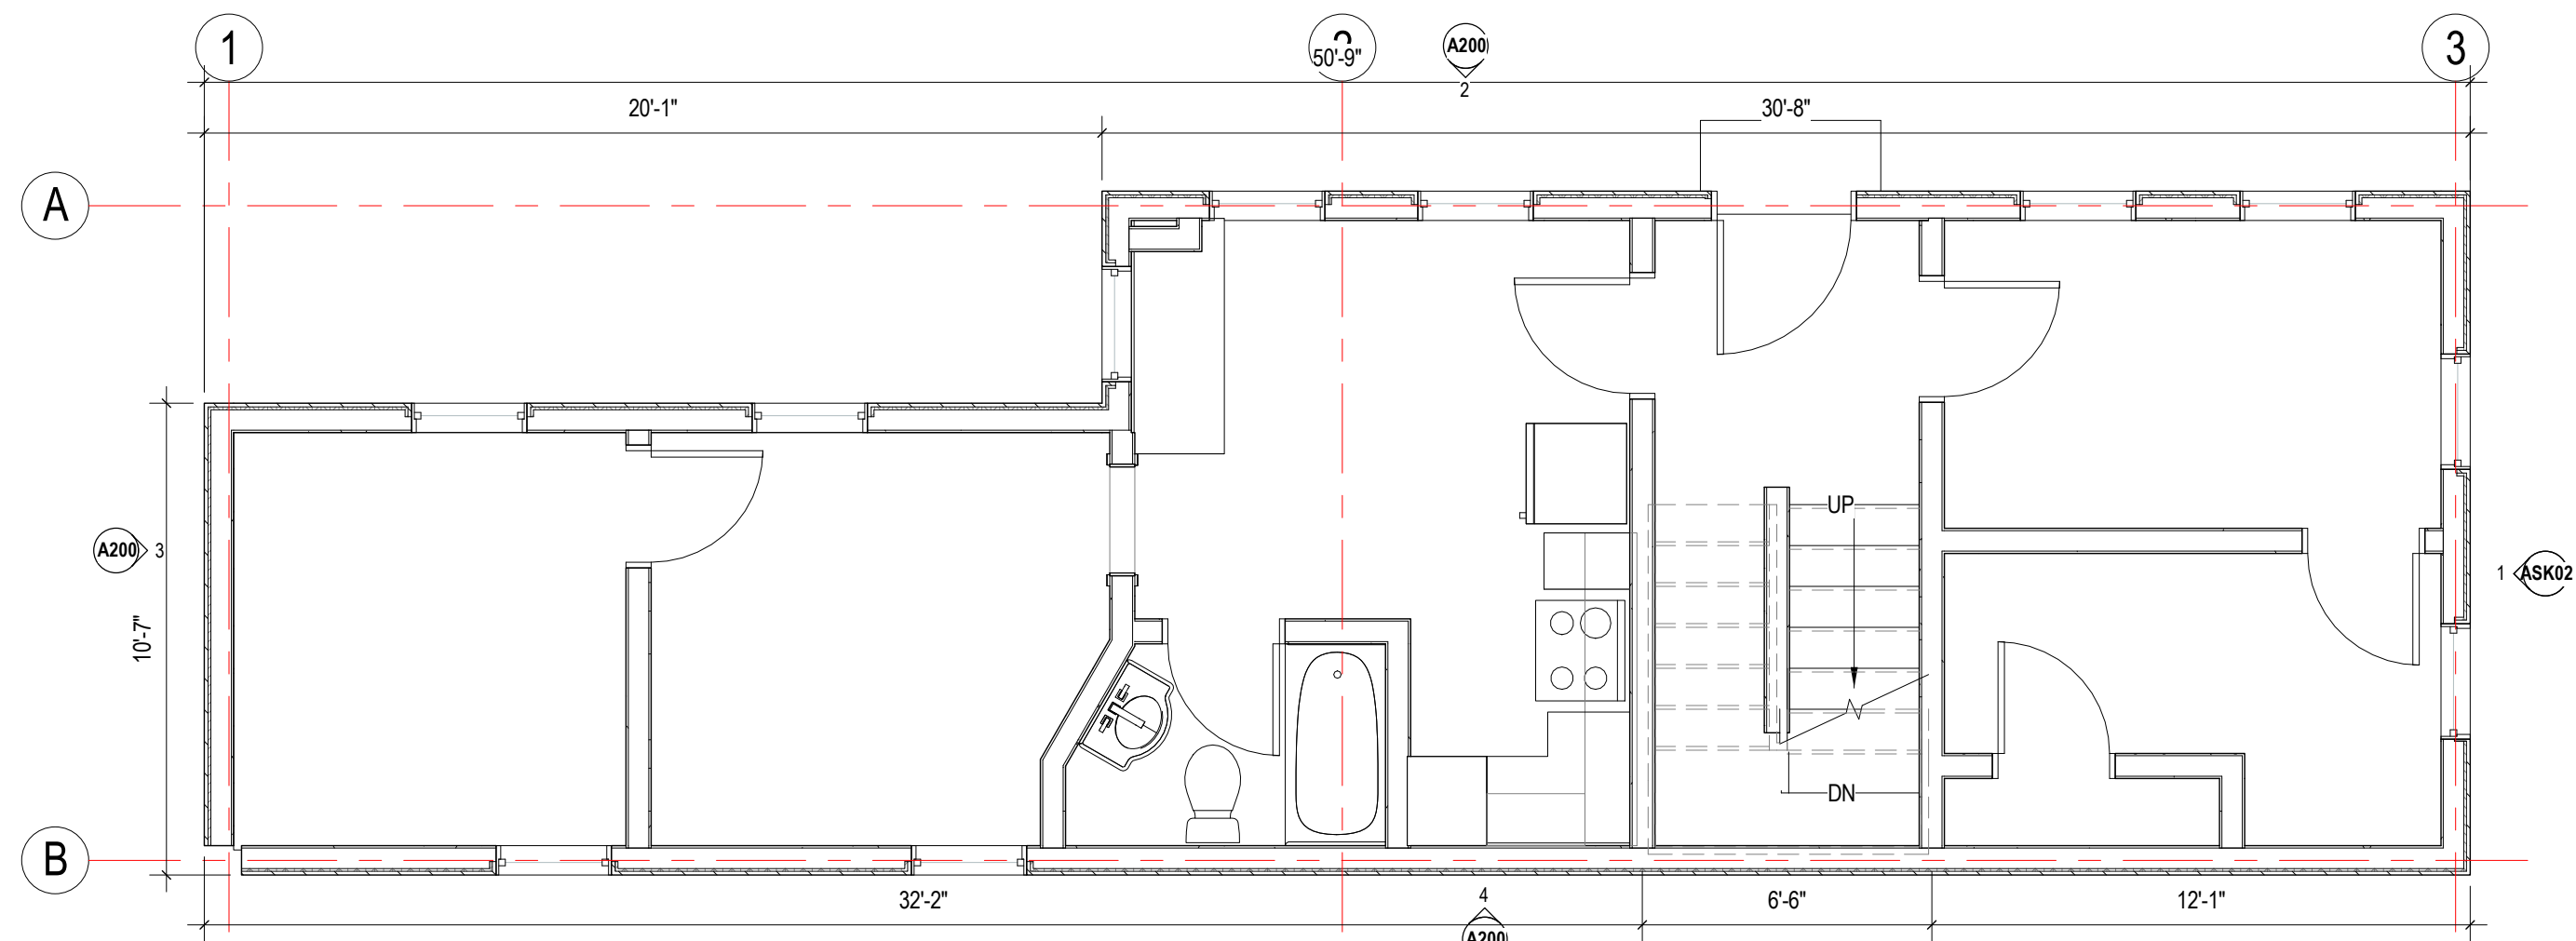


1 EXISTING FIRST FLOOR PLAN
1/4" = 1'-0"

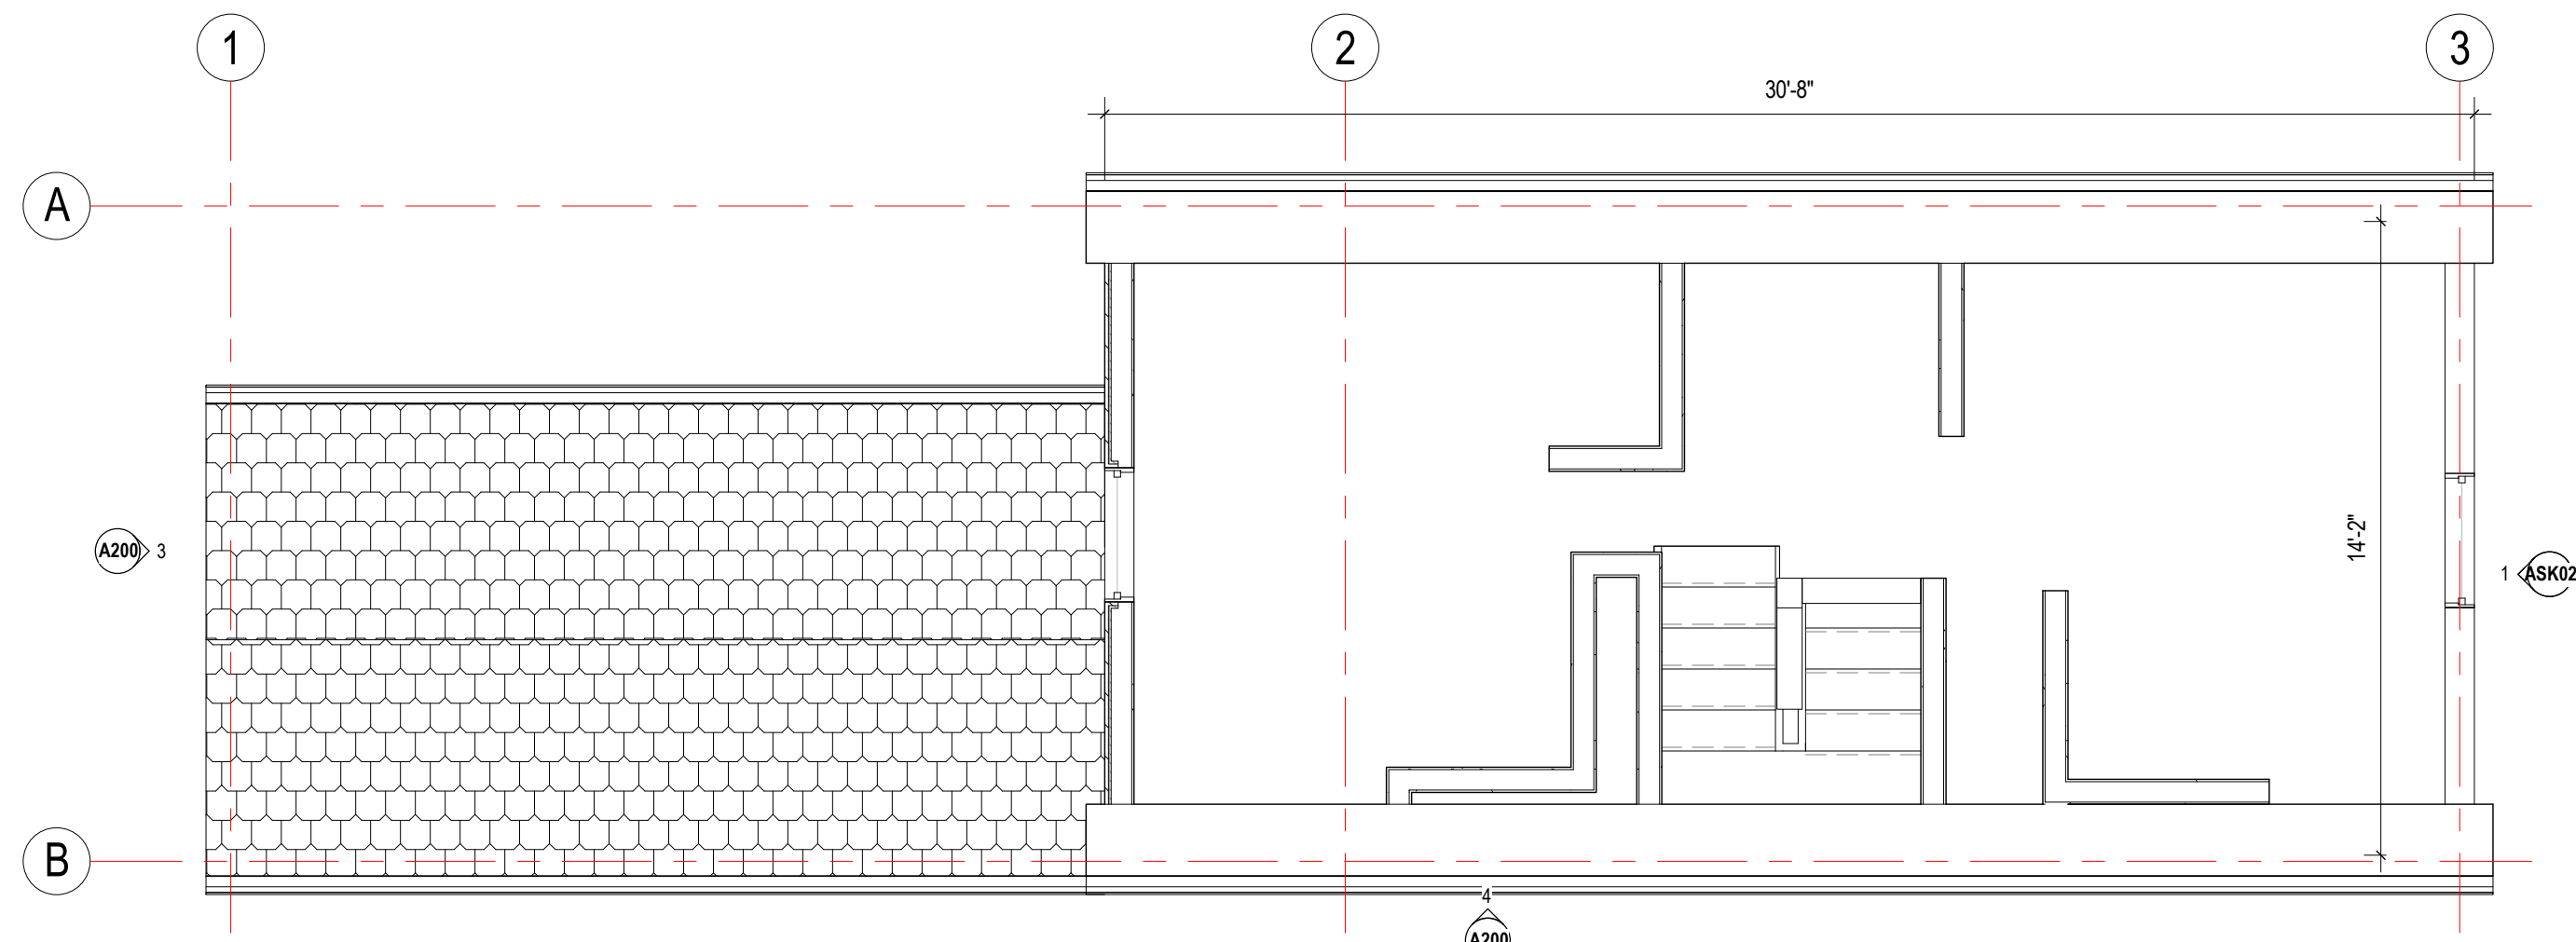


3 EXISTING THIRD FLOOR PLAN
1/4" = 1'-0"

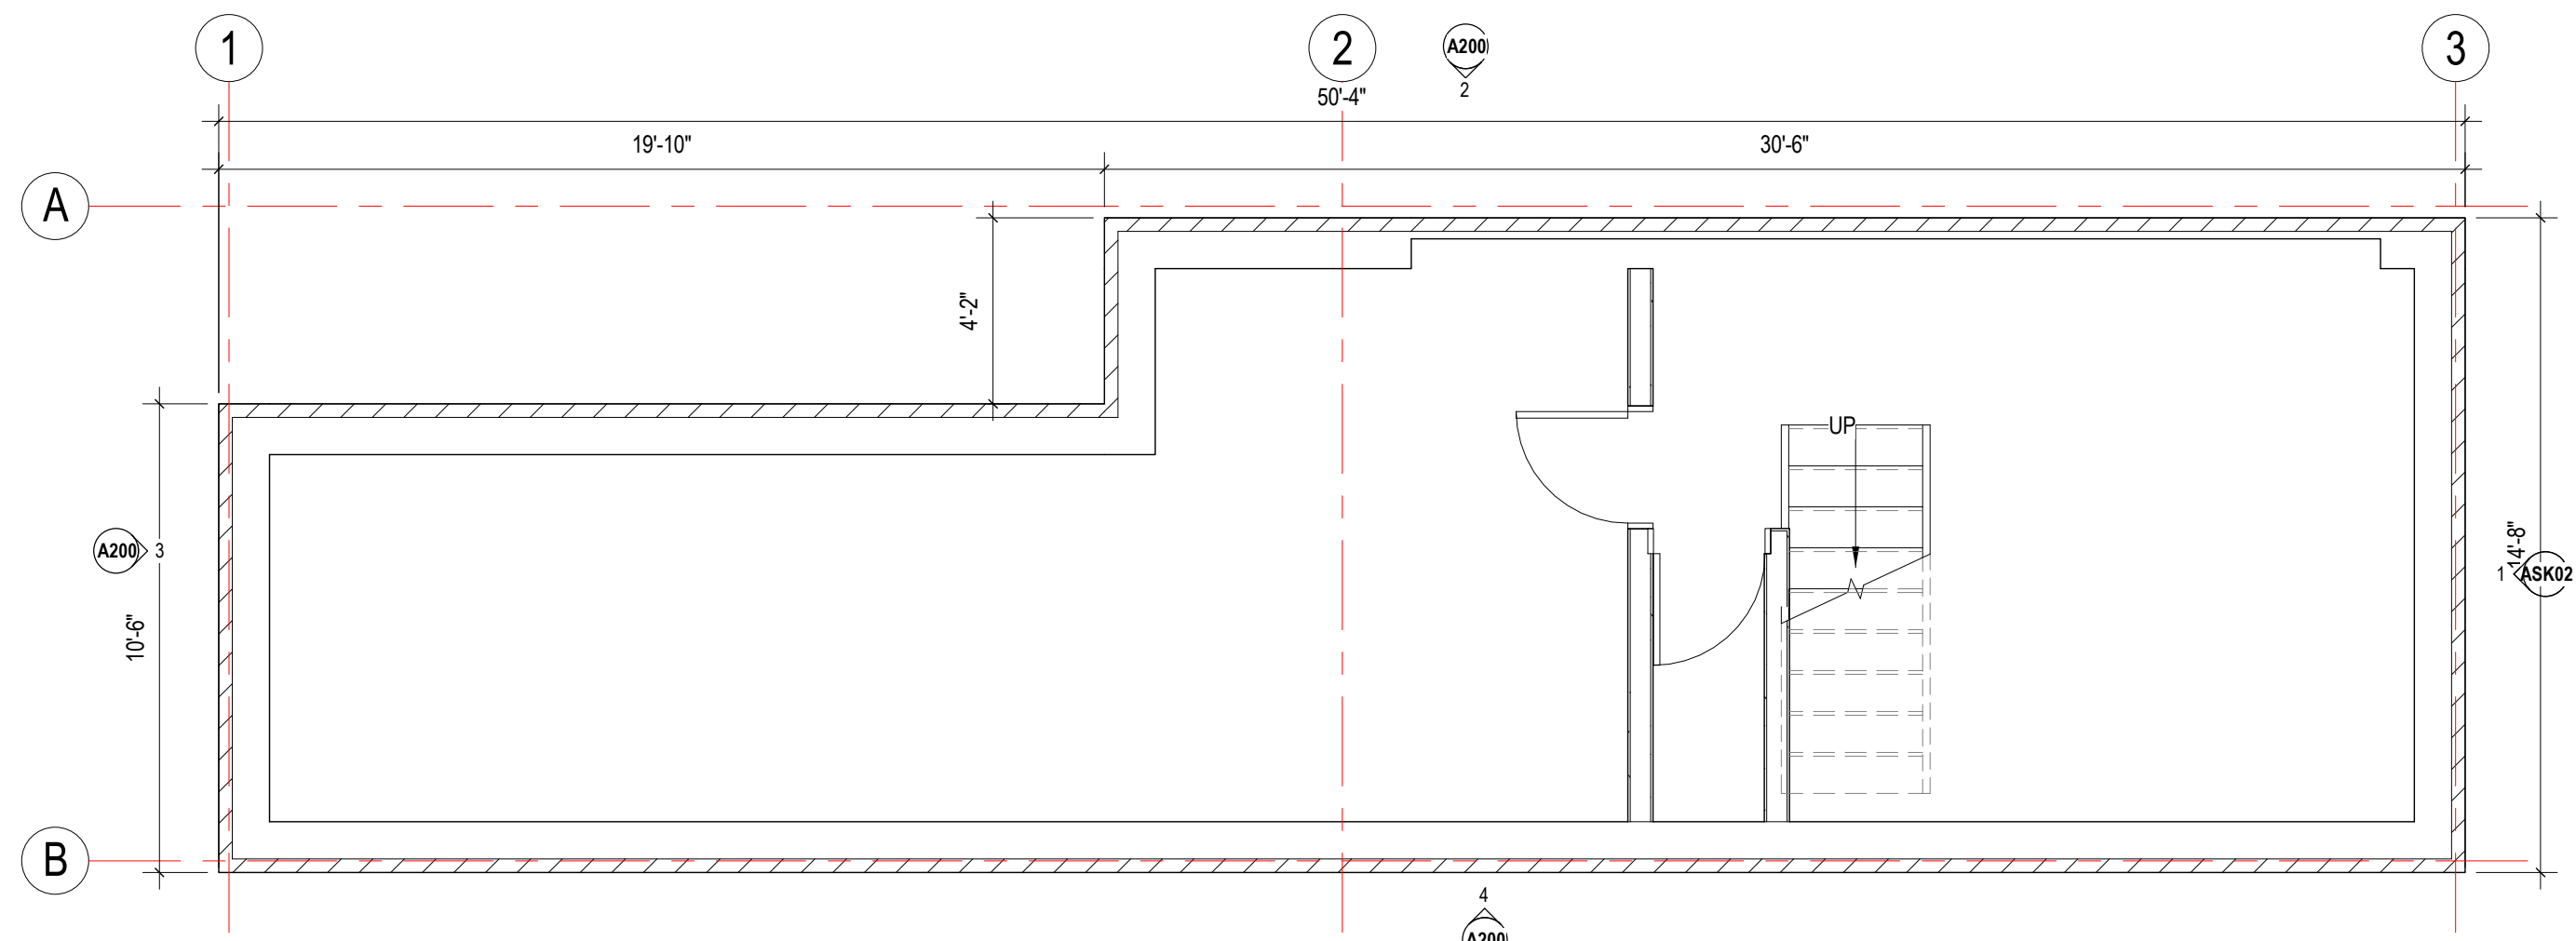

4 EXISTING BASEMENT FLOOR PLAN
1/4" = 1'-0"

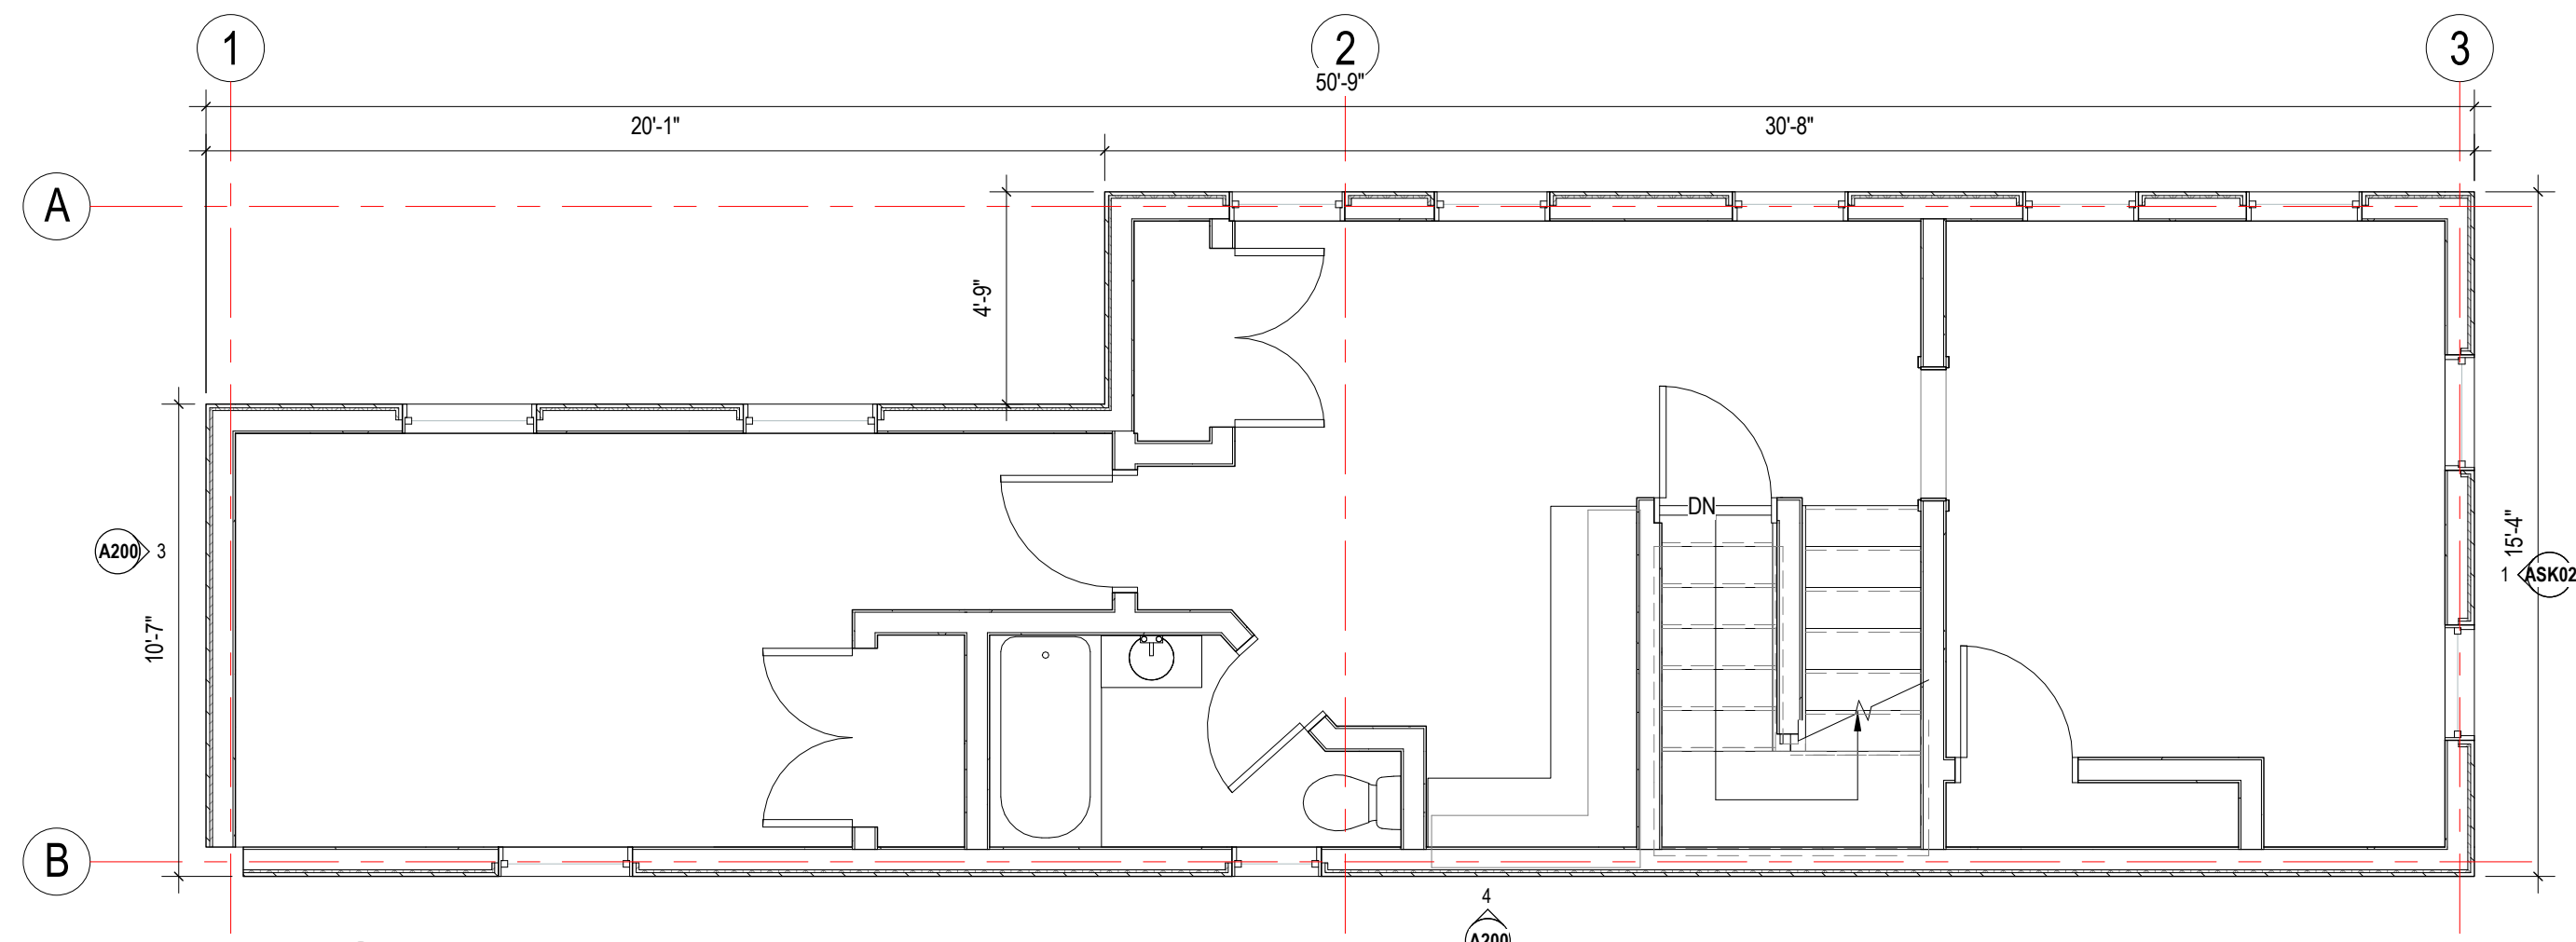

2 EXISTING SECOND FLOOR PLAN
1/4" = 1'-0"

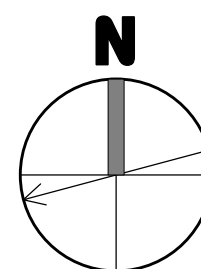

For Permit

WARNING:
Joe The Architect, Inc., all drawings and written material herein constitute the original and unpublished work of the architect, and the same may not be duplicated, used, or disclosed without the written consent of the architect. Contractors to use Architectural drawings for set out. Contractors to check and verify all Dimensions on Site prior to Construction/Fabrication. Figure Dimensions take precedence over Scaled Dimensions. Any discrepancies should be immediately referred to the Architect. The project manager shall be notified in writing of any discrepancies prior to proceeding with the work. The scale of drawings may change when copied or faxed. All work to comply with I.B.C. Regulations and relevant American Standards.
© 2019 - all rights reserved

consultant / contractor information:

stamp:



revision	revision description	date
1	SPECIAL PERMIT	03/26/2021

project title:
Gore Street Development

33 Gore Street, Cambridge, MA 2141

client information:
33 Gore LLC, c/o Koskores Real Estate Corp.
2 Lincoln Street, Somerville, MA 02145

J t A
JOE THE ARCHITECT
343 Medford Street, Suite 4C Somerville, MA 02145
t: +1(617) 764-3593 e: askjoe@joethearchitect.com
www.joethearchitect.com

drawing title
EXISTING FLOOR PLANS

project number 308	drawing scale 1/4" = 1'-0"	approver Approver
-----------------------	-------------------------------	----------------------

drawing number A030	revision 1
-------------------------------	---------------

NOT FOR CONSTRUCTION
3/26/2021 10:35:42 AM